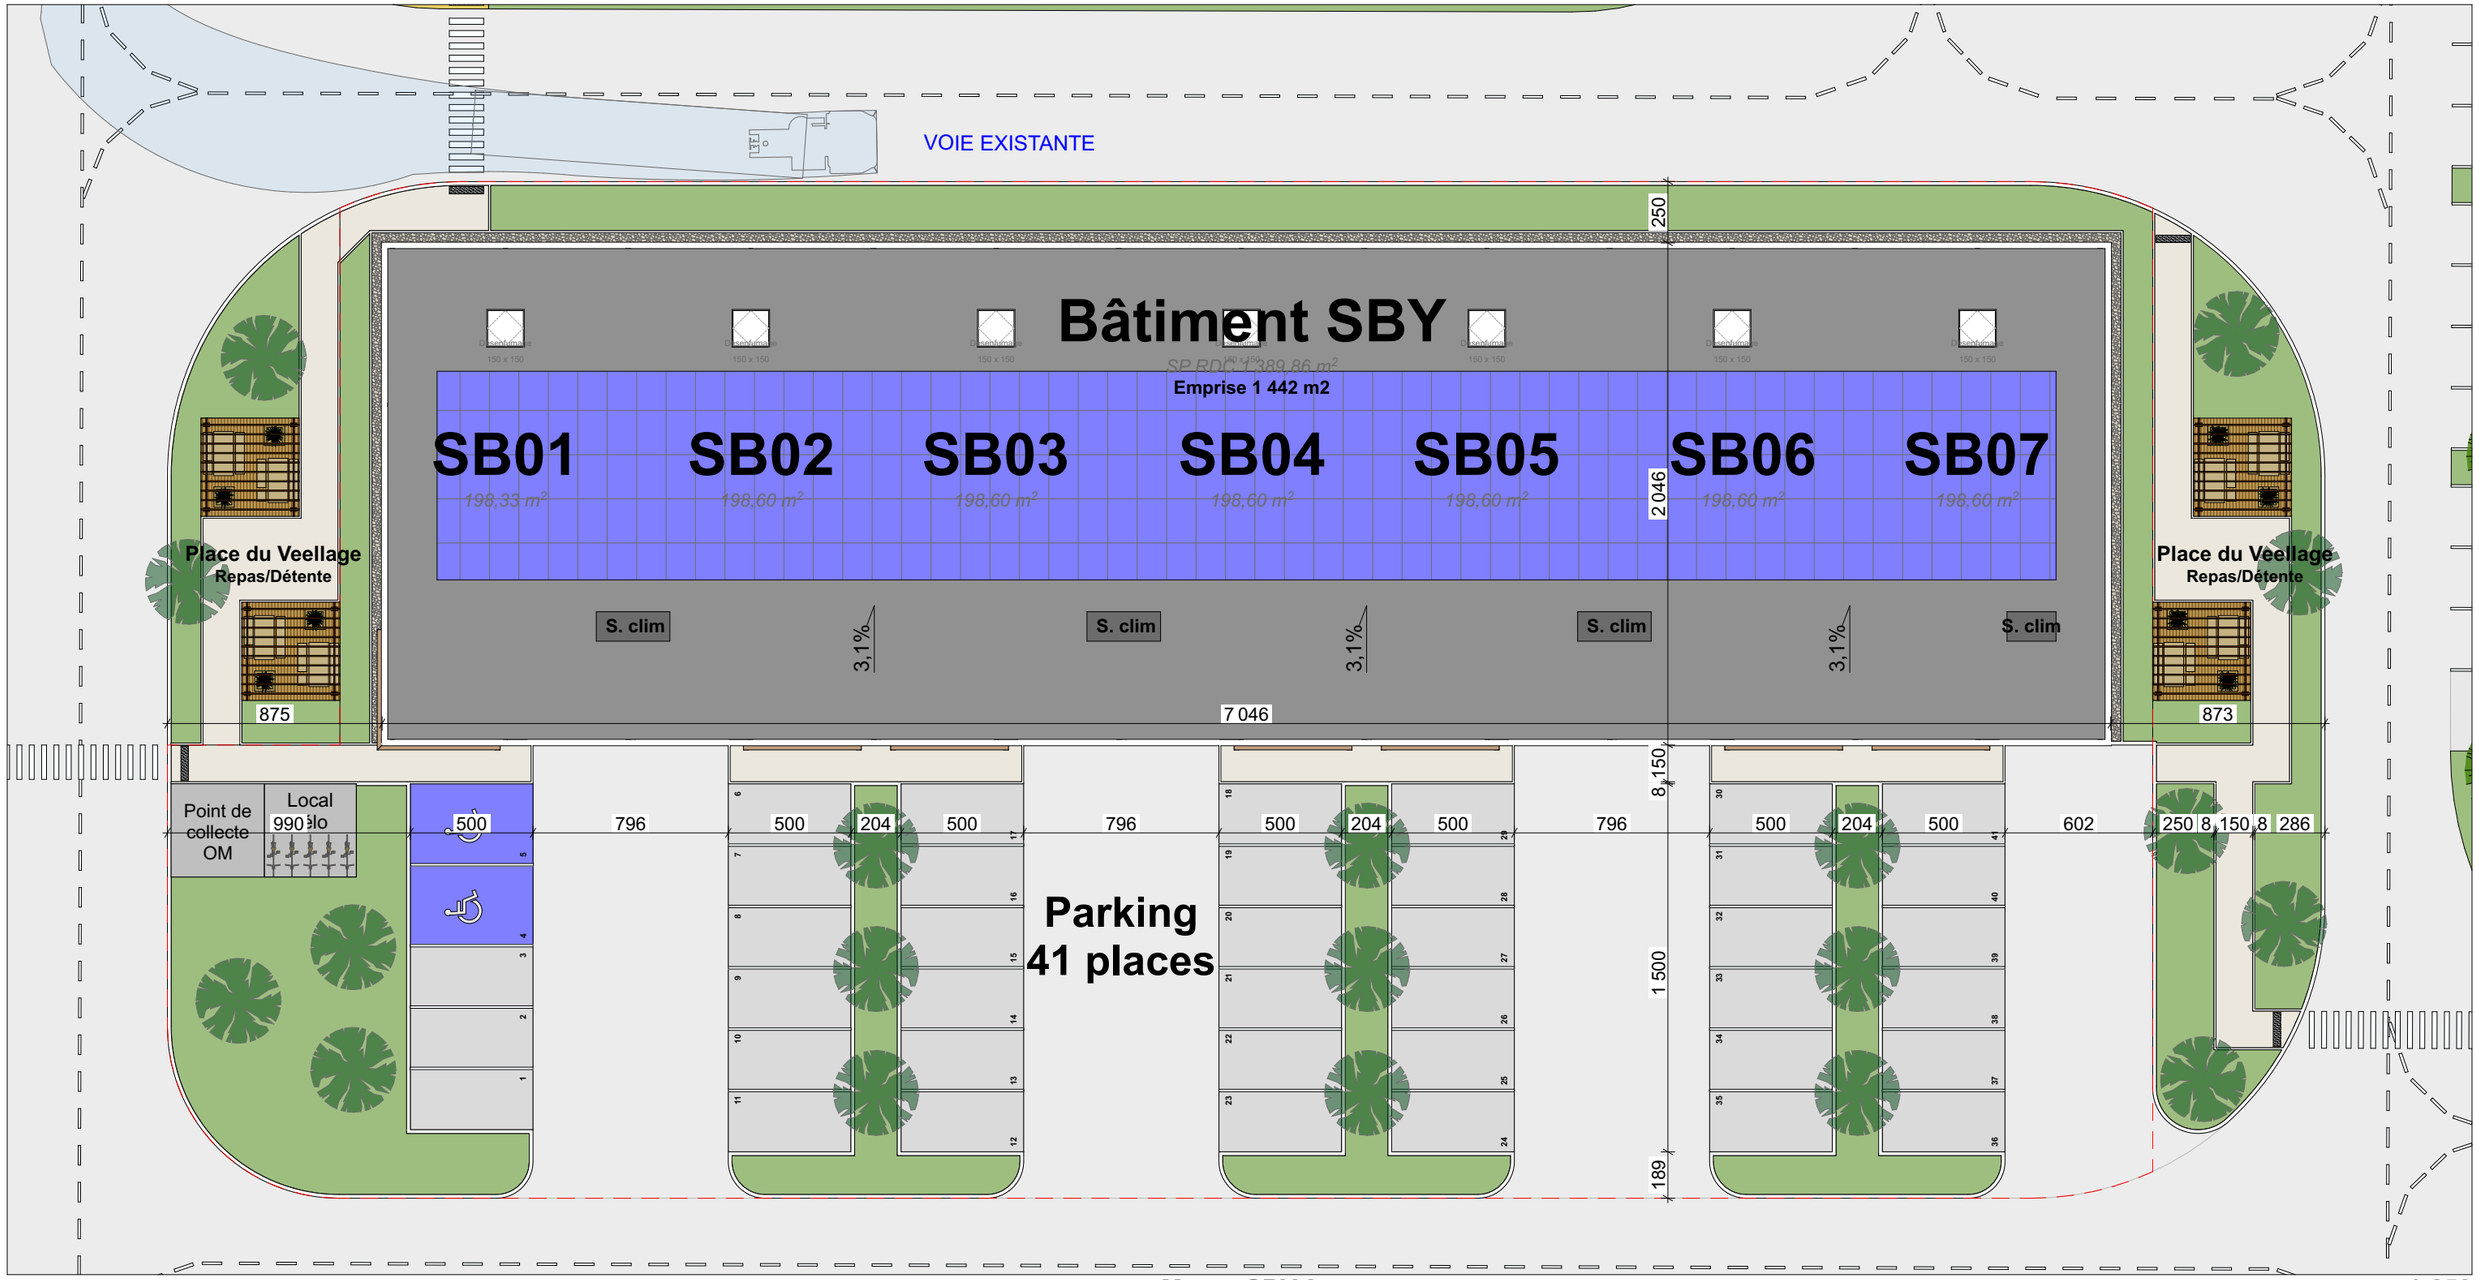

Masse SBY 2 1:250

Terrain	3 135 m²
Emprise au sol	1 389 m²
Bande stérile	47 m²
Béton désactivé	86 m²
Enrobé	557 m²
Enrobé drainant	554 m²
Espaces verts	502 m²

Buildconcept
Lieu dit Saint Vincent
81 140 CAHUZAC SUR VERE
05 62 212 212

VEELLAGE POITIERS

Rue Albin HALLER - 86 000POITIERS

DATE	ECHELLE		PHASE	PAGE
03/04/2026	1:250	Plan de masse	PC-01	

REFERENCE

SAS PARIS PROPERTIES DEVELOPPEMENT
M. Fabien ARZUR
7 Rue de l'Amiral d'Estaing
75 116PARIS Cedex 16

Ref : n° 347

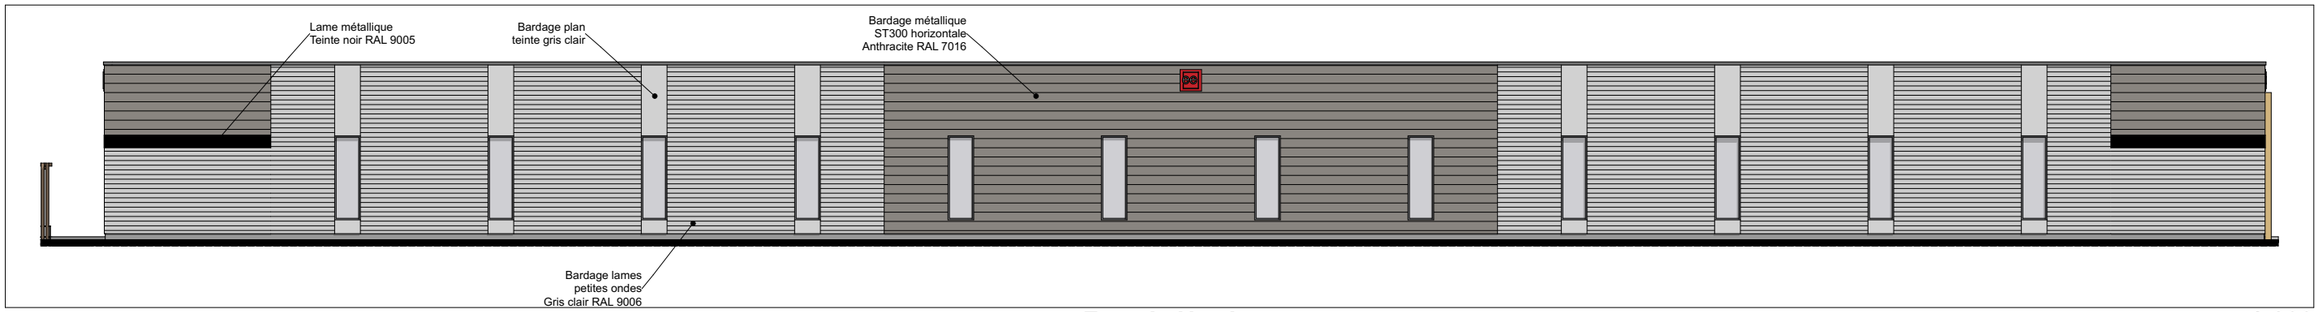

Façade Nord 1:200

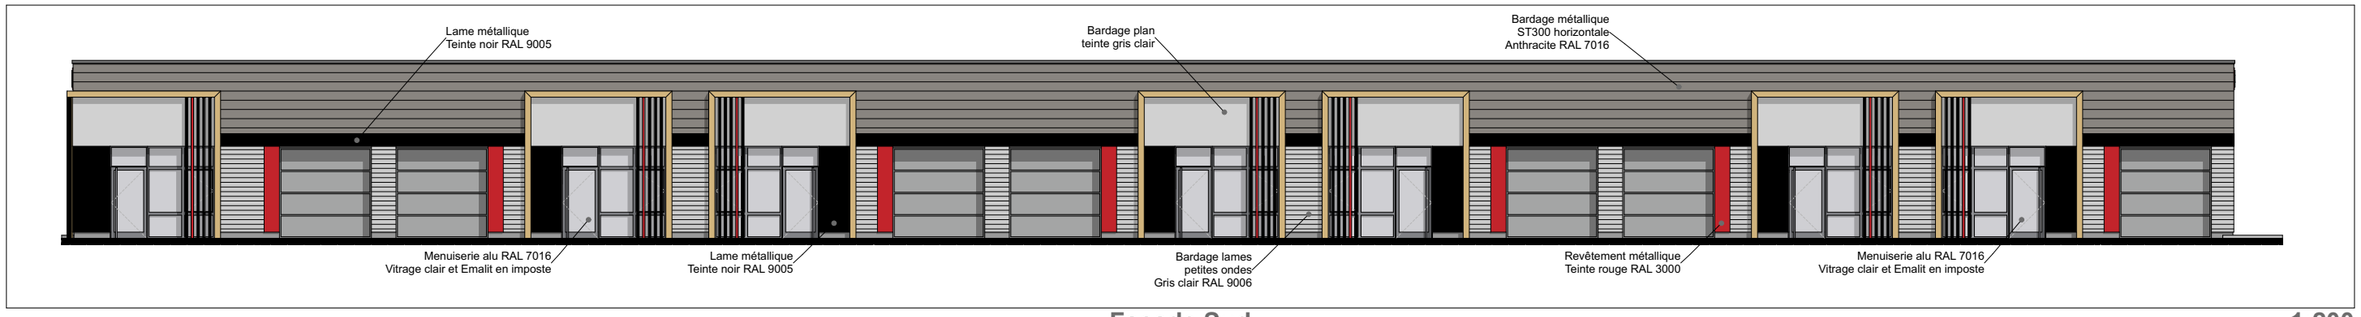

Façade Sud 1:200

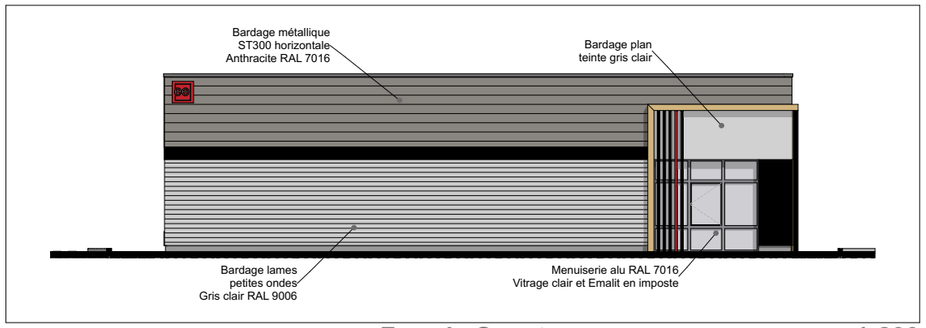

Façade Ouest 1:200

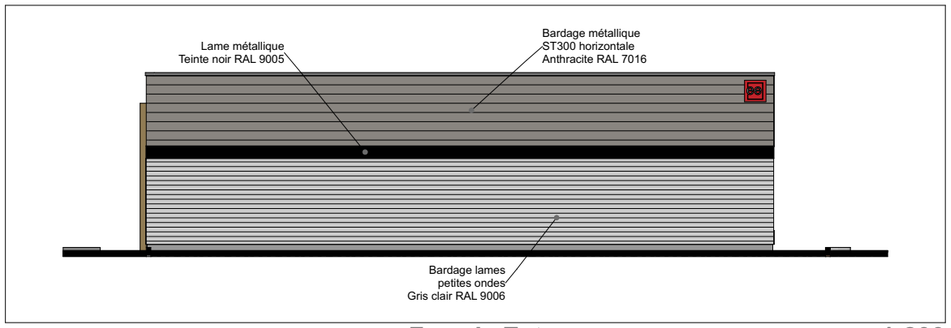

Façade Est 1:200

Buildconcept
Lieu dit Saint Vincent
81 140 CAHUZAC SUR VERE
05 62 212 212

VEELLAGE POITIERS

Rue Albin HALLER - 86 000POITIERS

DATE	ECHELLE		PHASE	PAGE
03/04/2026	1:200	Façades	PC-01	

REFERENCE

SAS PARIS PROPERTIES DEVELOPPEMENT
M. Fabien ARZUR
7 Rue de l'Amiral d'Estaing
75 116PARIS Cedex 16

Ref : n° 347

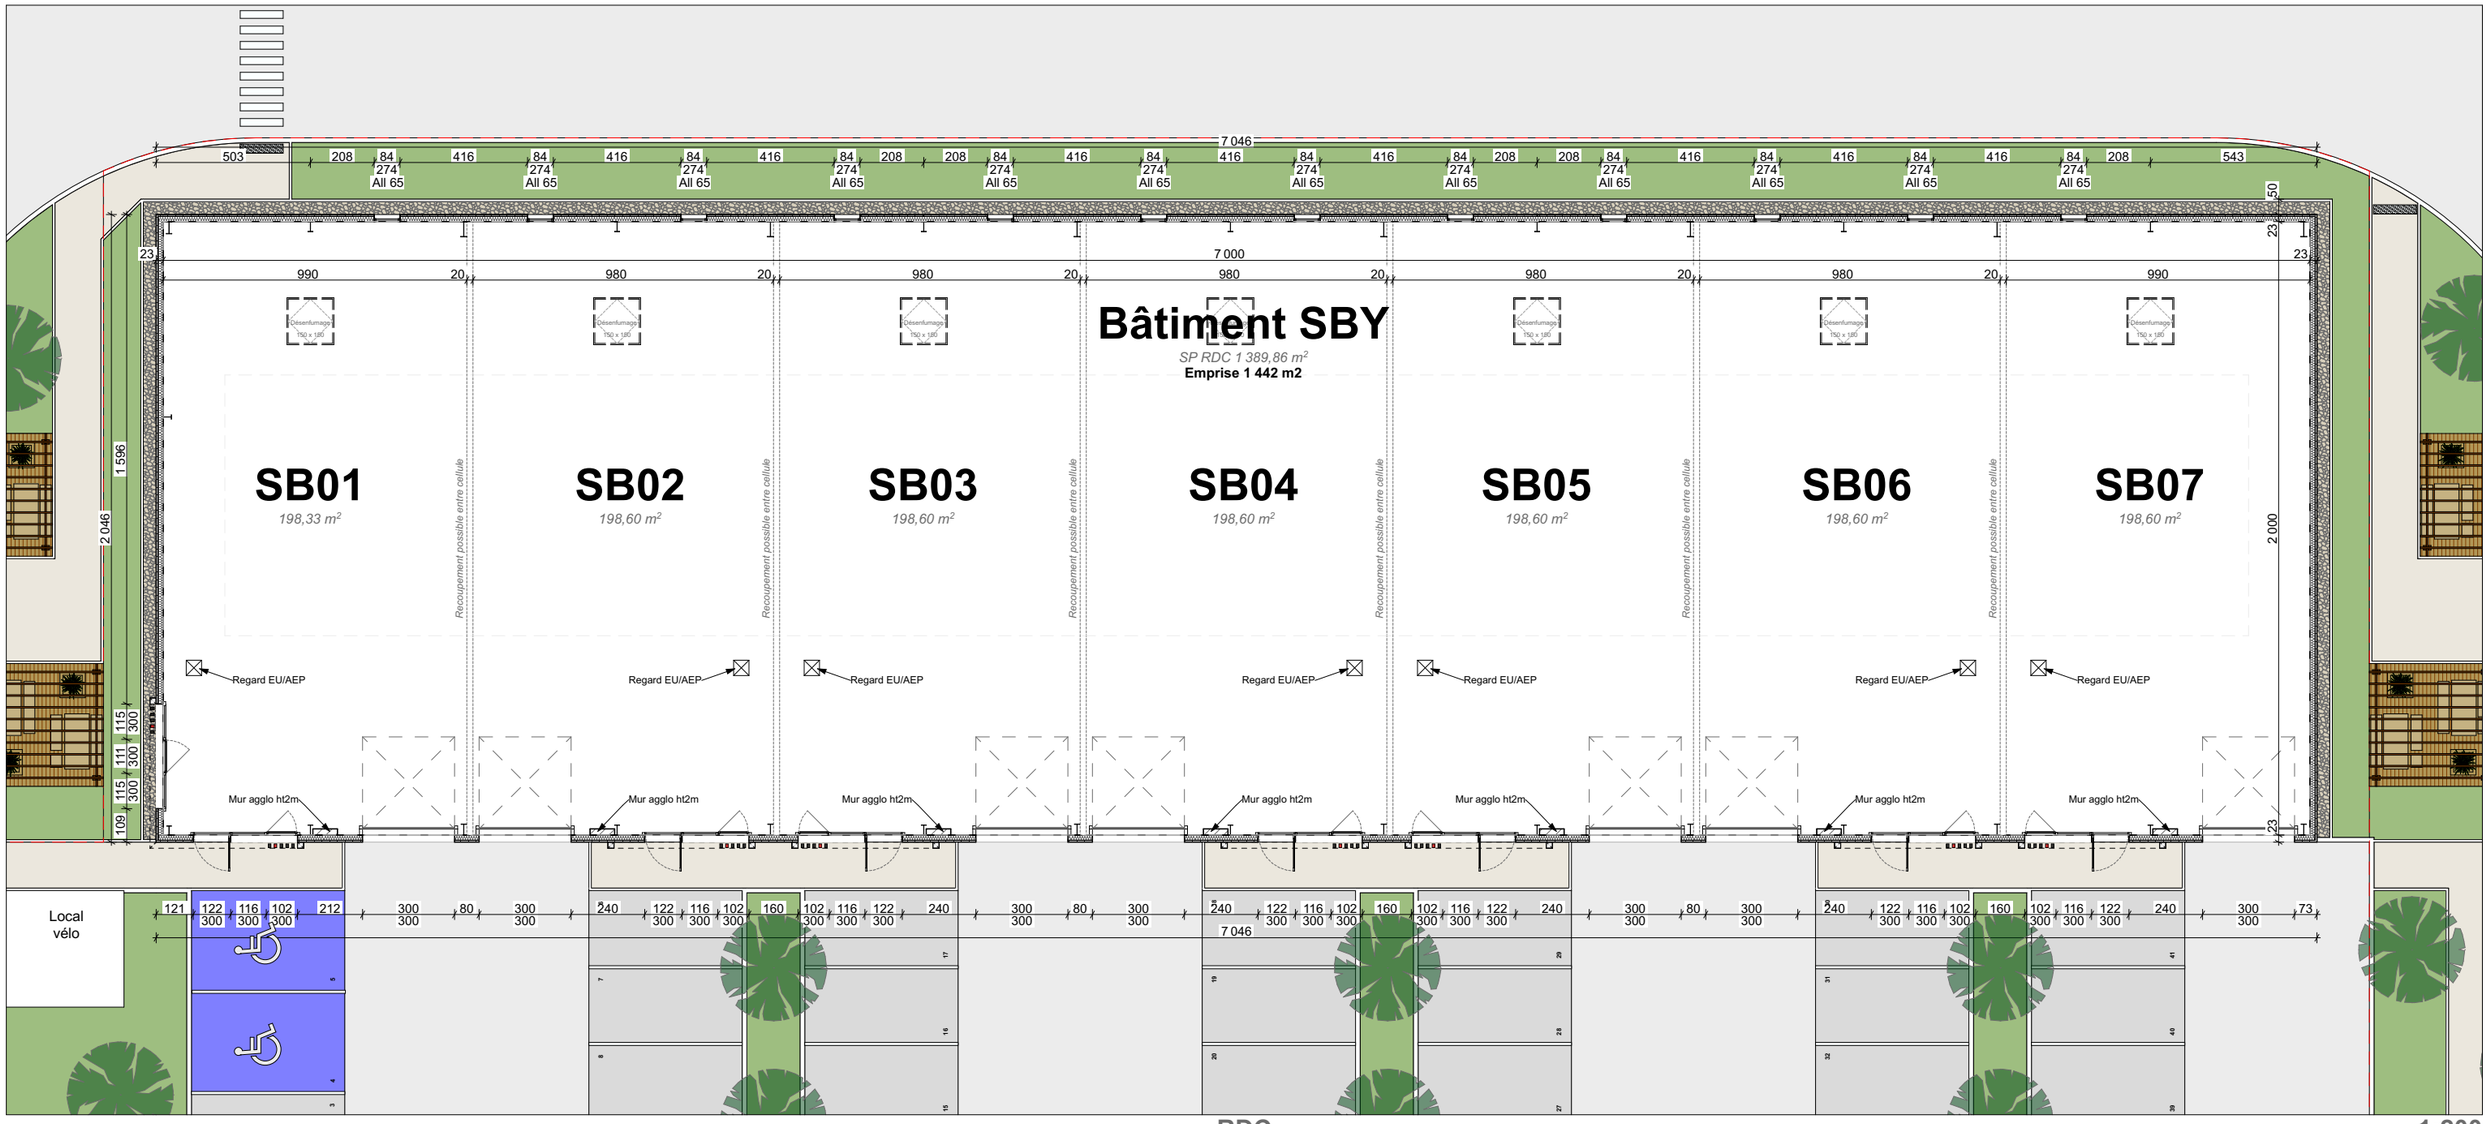

RDC 1:200

A Surface de plancher	
Cellule	Superficie mesurée
SB01	198,33
SB02	198,60
SB03	198,60
SB04	198,60
SB05	198,60
SB06	198,60
SB07	198,60
	1 389,93 m²

Buildconcept
Lieu dit Saint Vincent
81 140 CAHUZAC SUR VERE
05 62 212 212

VEELLAGE POITIERS

Rue Albin HALLER - 86 000POITIERS

DATE	ECHELLE		PHASE	PAGE
03/04/2026	**1:200**	**Vue en plan**	**PC-01**	

REFERENCE

SAS PARIS PROPERTIES DEVELOPPEMENT
M. Fabien ARZUR
7 Rue de l'Amiral d'Estaing
75 116PARIS Cedex 16

Ref : n° 347