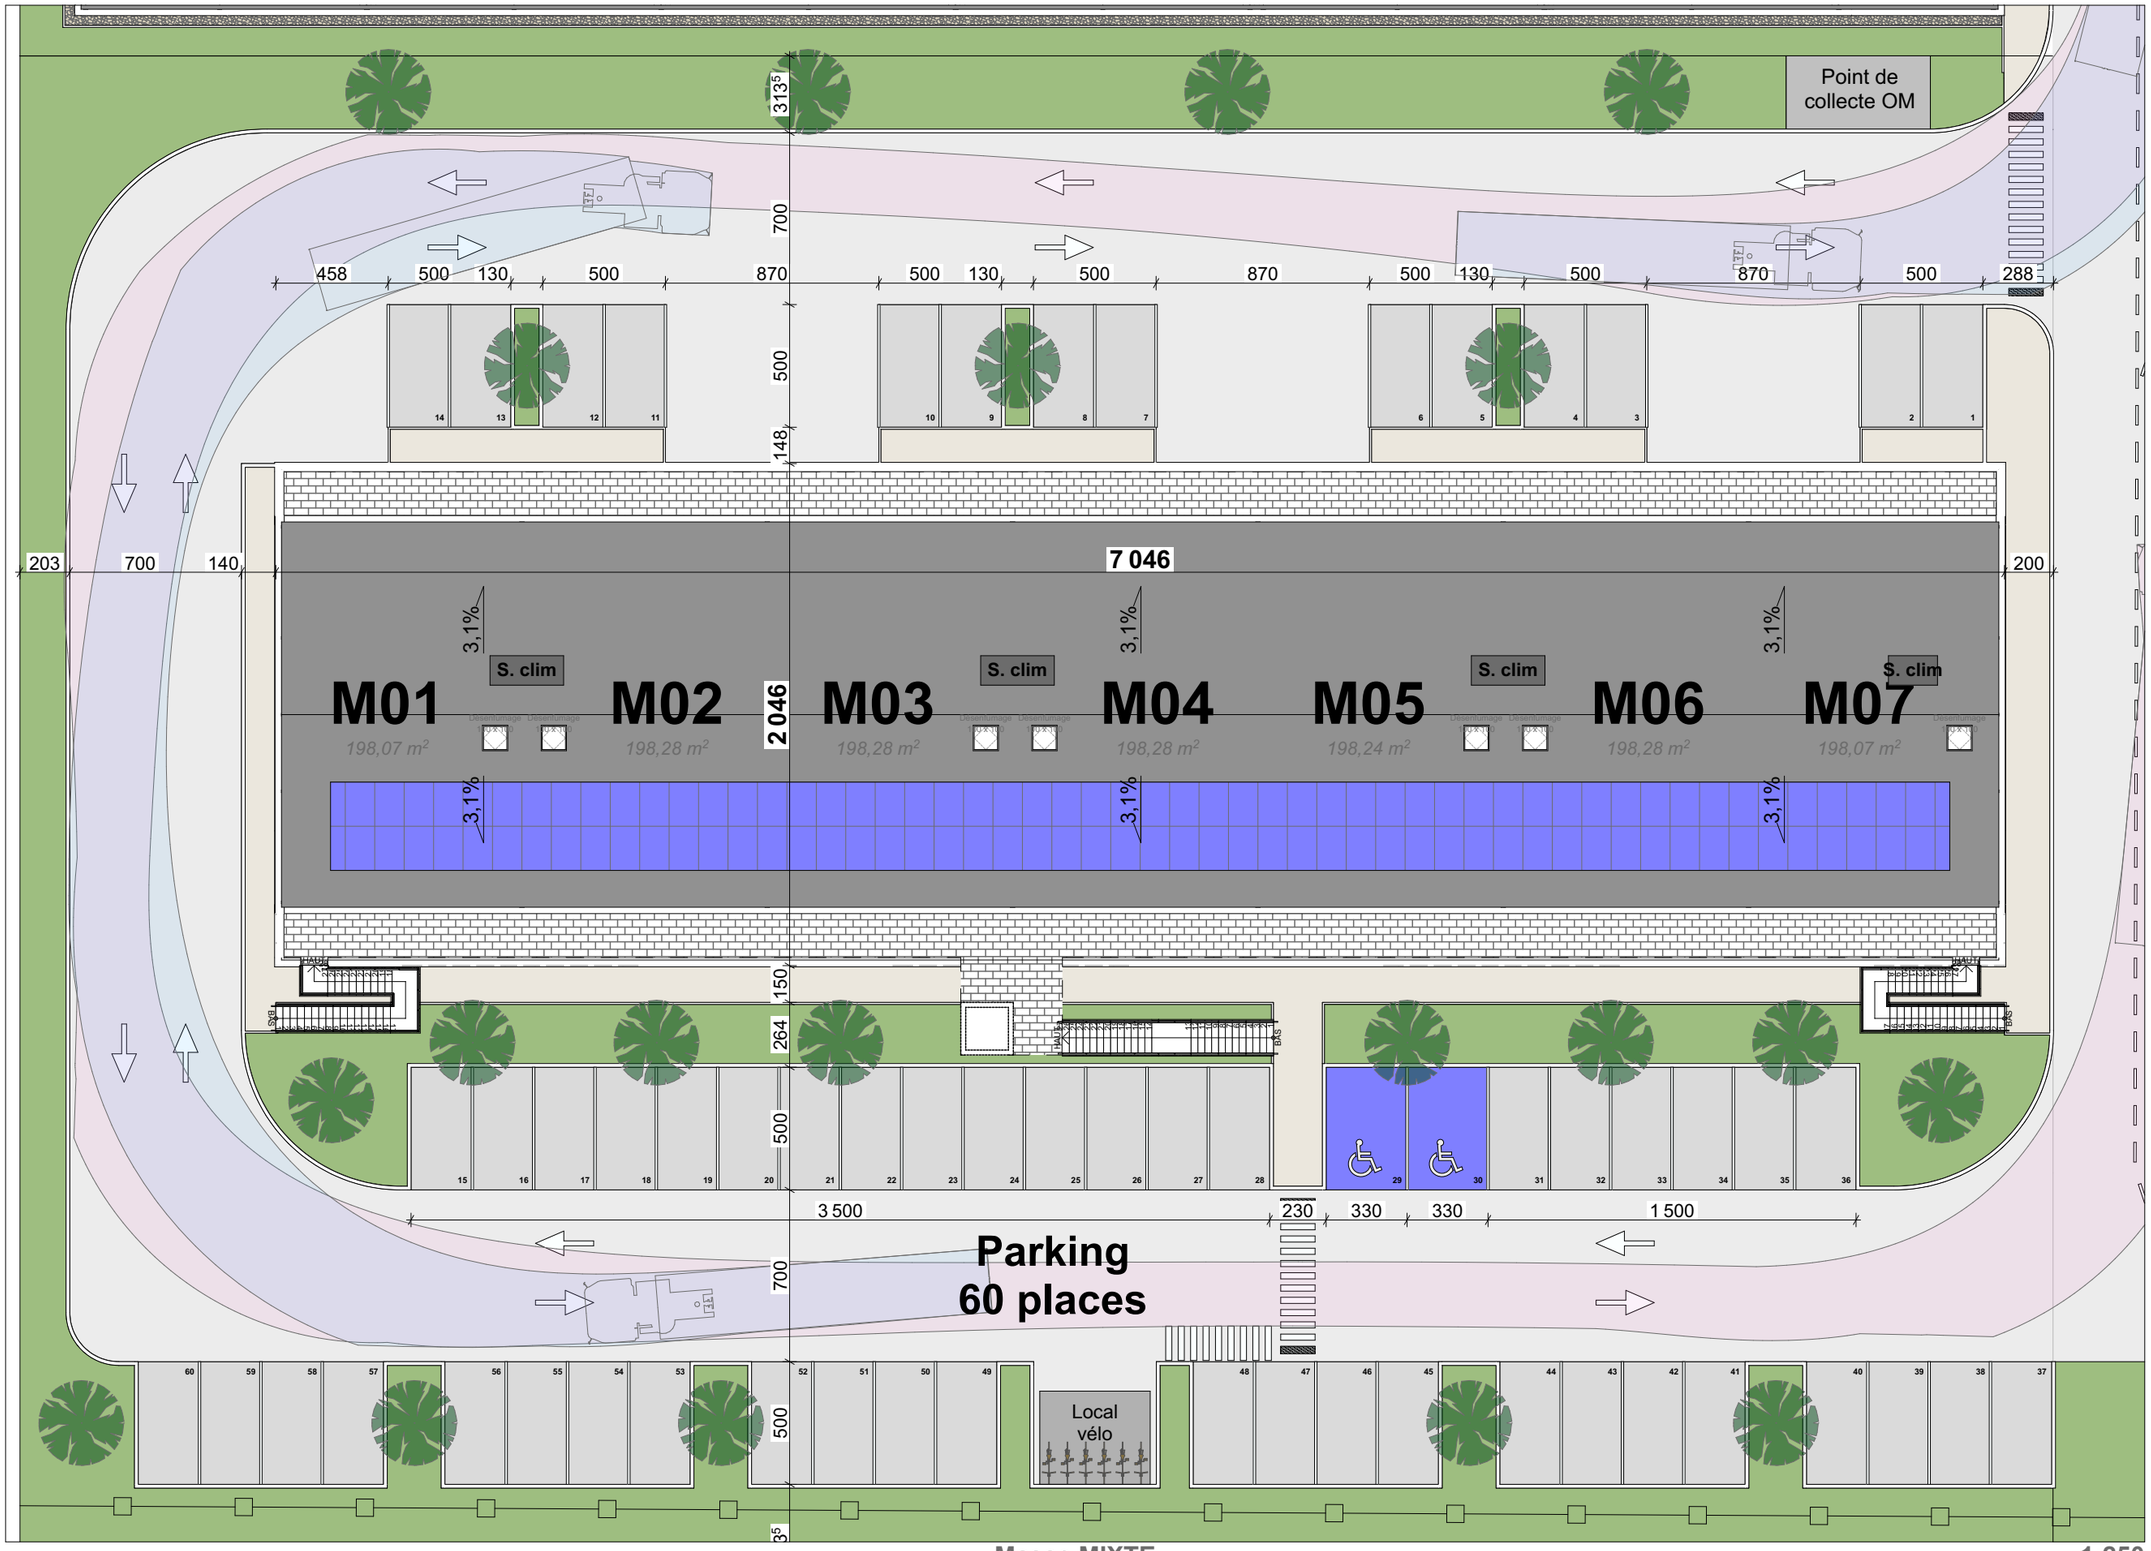

Terrain	**5 336 m²**
Emprise au sol	1 446 m²
Béton désactivé	263 m²
Enrobé	1 626 m²
Enrobé drainant	725 m²
Espaces verts	1 276 m²

Masse MIXTE

1:250

Buildconcept
Lieu dit Saint Vincent
81 140 CAHUZAC SUR VERE
05 62 212 212

VEELLAGE POITIERS

Rue Albin HALLER - 86 000POITIERS

DATE	ECHELLE		PHASE	PAGE
03/04/2026	1:250	Plan de masse	PC-01	

REFERENCE

SAS PARIS PROPERTIES DEVELOPPEMENT
M. Fabien ARZUR
7 Rue de l'Amiral d'Estaing
75 116PARIS Cedex 16

Ref : n° 347

Façade Sud 1:200

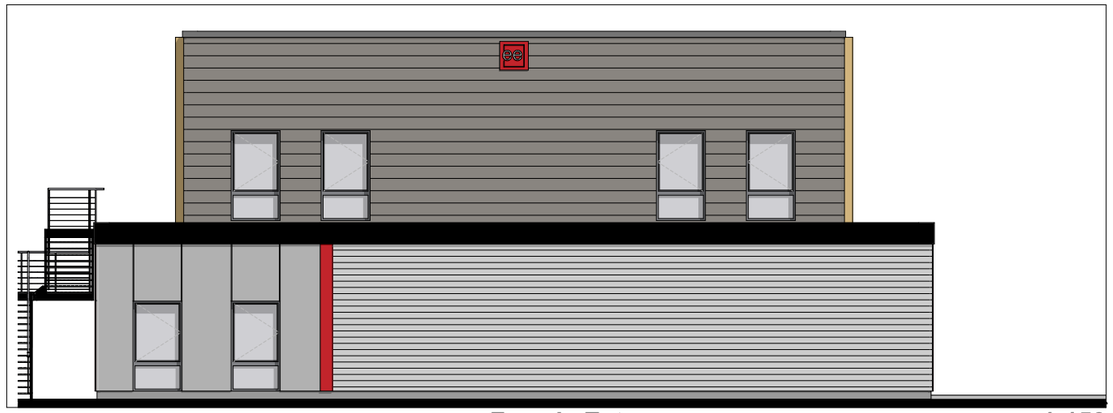

Façade Est 1:150

Façade Ouest 1:150

Façade Nord 1:200

Buildconcept
Lieu dit Saint Vincent
81 140 CAHUZAC SUR VERE
05 62 212 212

VEELLAGE POITIERS

Rue Albin HALLER - 86 000POITIERS

DATE	ECHELLE		PHASE	PAGE
03/04/2026	1:150, 1:200	Façades	PC-01	

REFERENCE

SAS PARIS PROPERTIES DEVELOPPEMENT
M. Fabien ARZUR
7 Rue de l'Amiral d'Estaing
75 116PARIS Cedex 16

Ref : n° 347

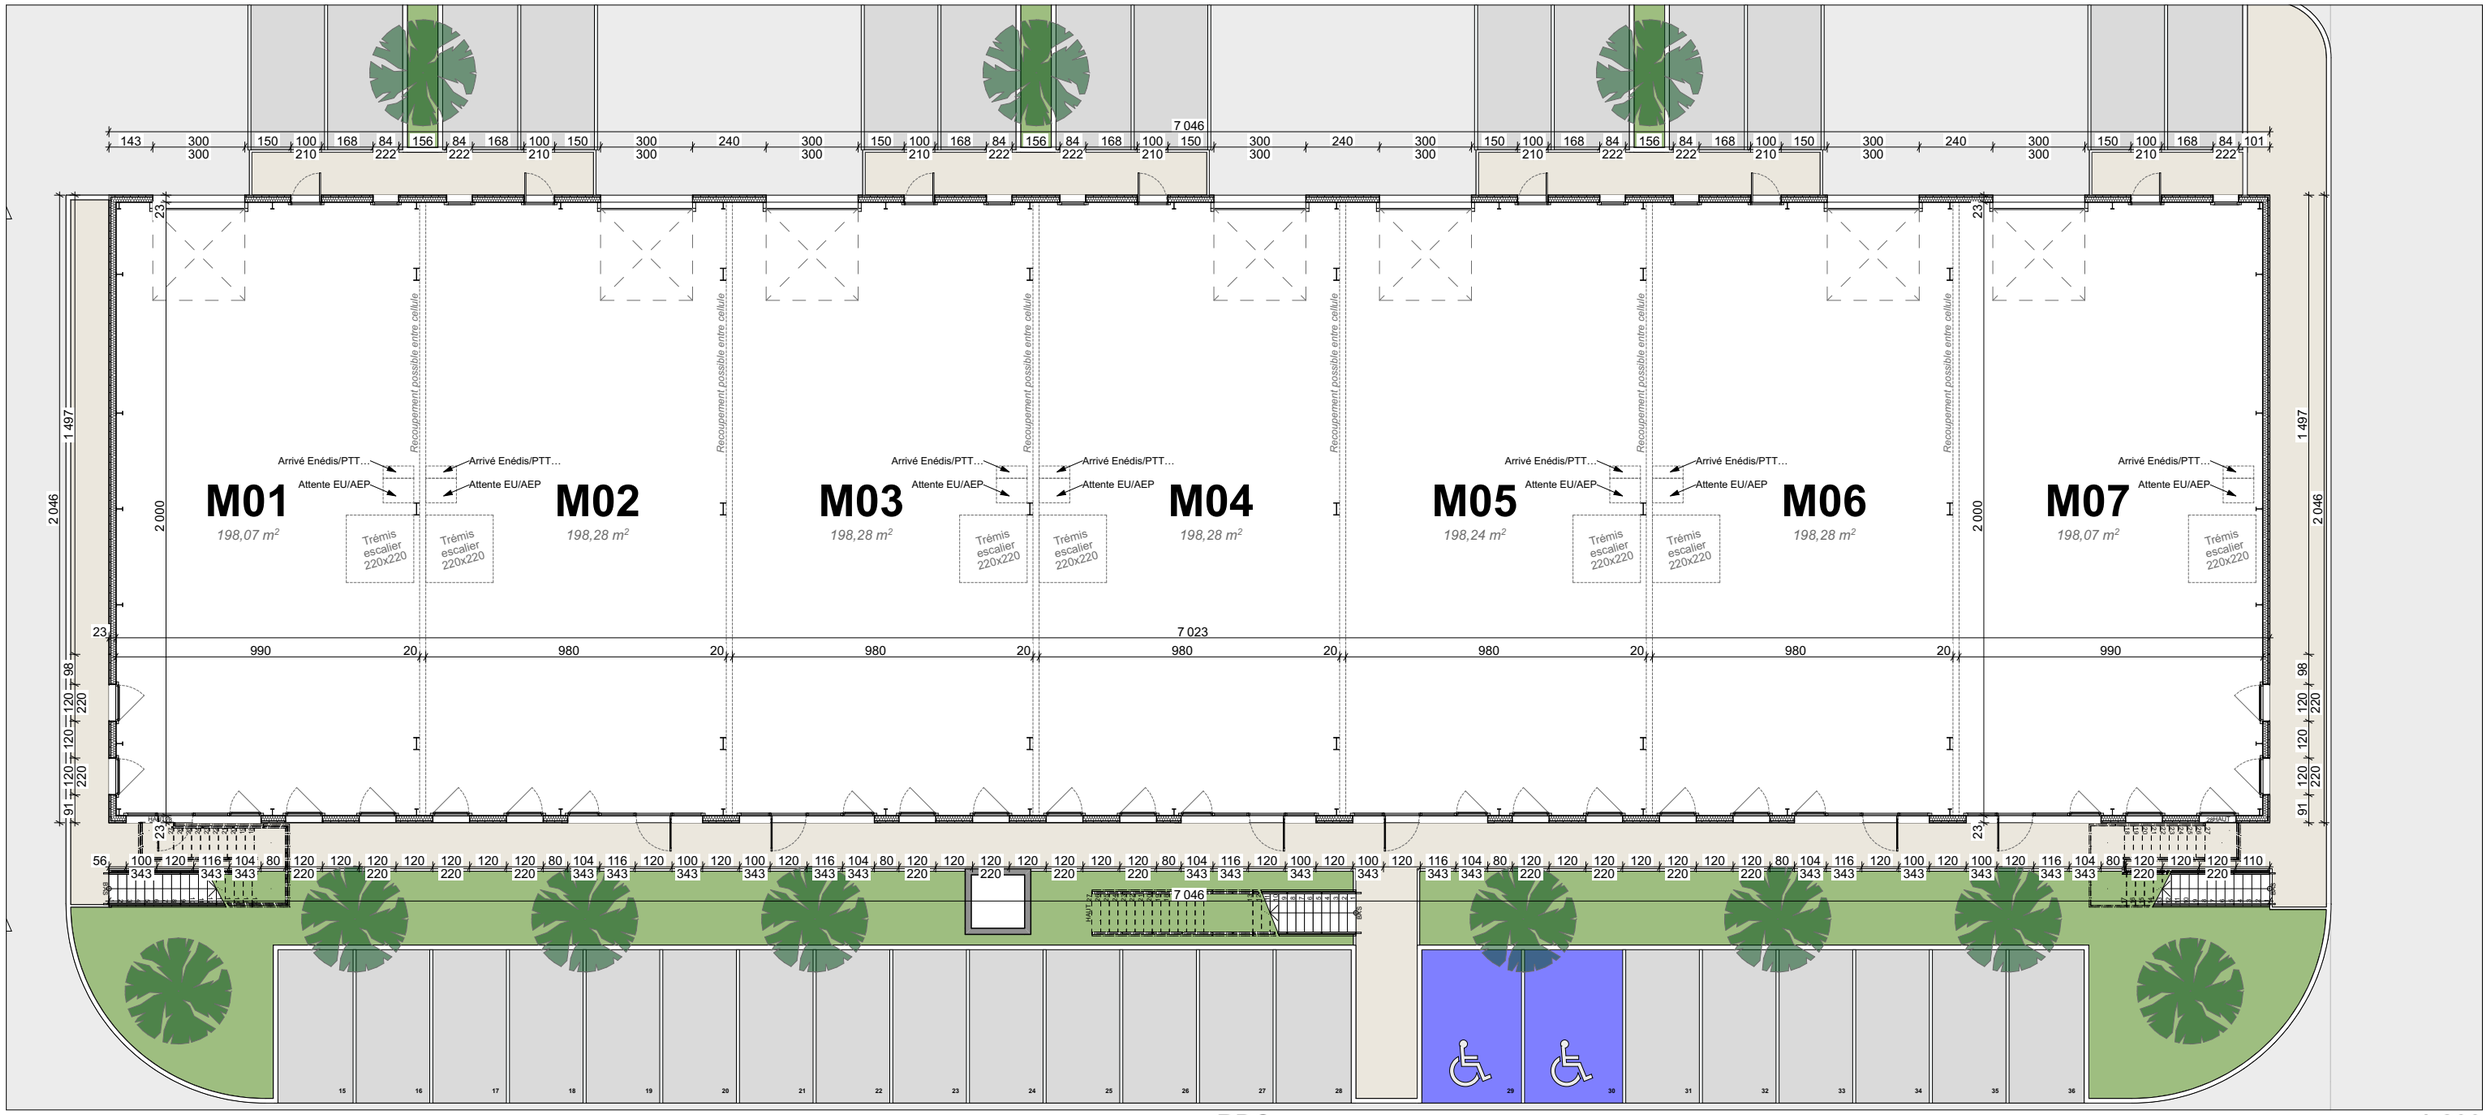

RDC

1:200

A MIXTE SP cellule		
Cellule	Etage	Superficie mesurée
M01	Rez-de-chaussée	198,07
M01	Etage mixte	155,56
		353,63 m²
M02	Rez-de-chaussée	198,28
M02	Etage mixte	155,99
		354,27 m²
M03	Rez-de-chaussée	198,28
M03	Etage mixte	155,99
		354,27 m²
M04	Rez-de-chaussée	198,28
M04	Etage mixte	155,99
		354,27 m²
M05	Rez-de-chaussée	198,24
M05	Etage mixte	155,99
		354,23 m²
M06	Rez-de-chaussée	198,28
M06	Etage mixte	155,99
		354,27 m²
M07	Rez-de-chaussée	198,07
M07	Etage mixte	155,56
		353,63 m²
		2 478,57 m²

REFERENCE

Buildconcept
Lieu dit Saint Vincent
81 140 CAHUZAC SUR VERE
05 62 212 212

VEELLAGE POITIERS

Rue Albin HALLER - 86 000POITIERS

DATE	ECHELLE		PHASE	PAGE
03/04/2026	1:200	RDC	PC-01	

SAS PARIS PROPERTIES DEVELOPPEMENT
M. Fabien ARZUR
7 Rue de l'Amiral d'Estaing
75 116PARIS Cedex 16

Ref : n° 347

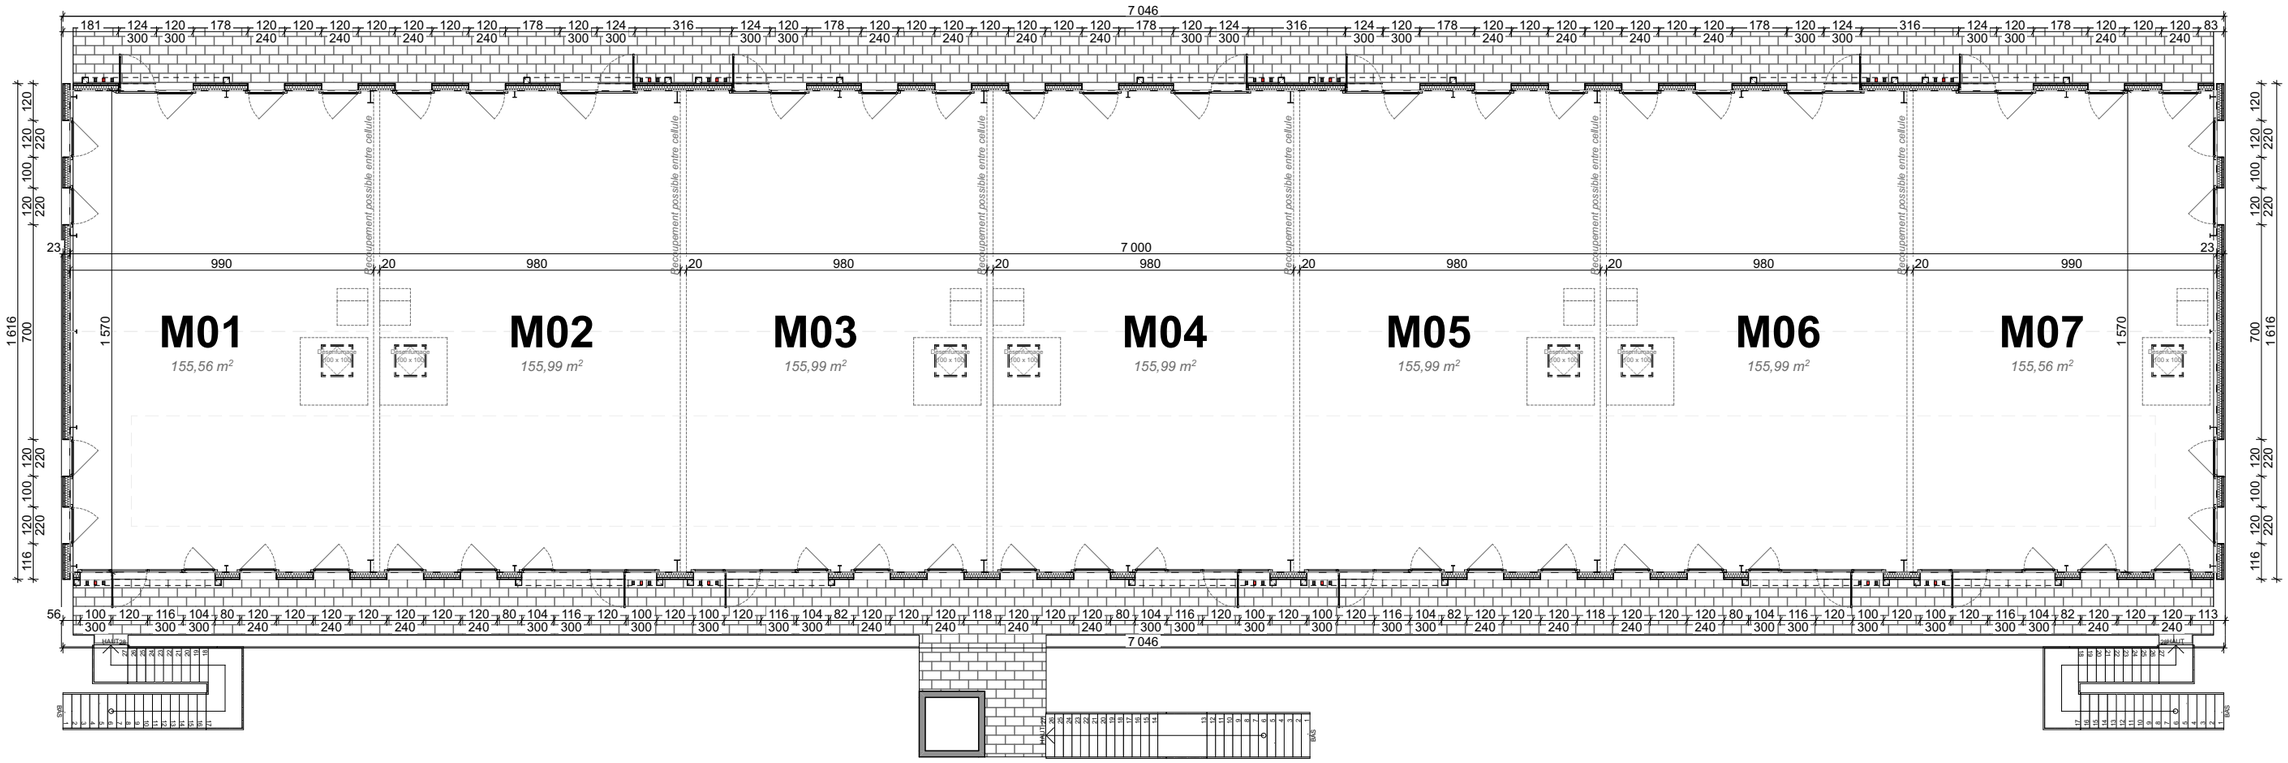

R+1 Mixte

1:200

A MIXTE SP cellule		
Cellule	Etage	Superficie mesurée
M01	Rez-de-chaussée	198,07
M01	Etage mixte	155,56
		353,63 m²
M02	Rez-de-chaussée	198,28
M02	Etage mixte	155,99
		354,27 m²
M03	Rez-de-chaussée	198,28
M03	Etage mixte	155,99
		354,27 m²
M04	Rez-de-chaussée	198,28
M04	Etage mixte	155,99
		354,27 m²
M05	Rez-de-chaussée	198,24
M05	Etage mixte	155,99
		354,23 m²
M06	Rez-de-chaussée	198,28
M06	Etage mixte	155,99
		354,27 m²
M07	Rez-de-chaussée	198,07
M07	Etage mixte	155,56
		353,63 m²
		2 478,57 m²

REFERENCE

Buildconcept
Lieu dit Saint Vincent
81 140 CAHUZAC SUR VERE
05 62 212 212

VEELLAGE POITIERS

Rue Albin HALLER - 86 000POITIERS

DATE	ECHELLE		PHASE	PAGE
03/04/2026	**1:200**	**R+1**	**PC-01**	

SAS PARIS PROPERTIES DEVELOPPEMENT
M. Fabien ARZUR
7 Rue de l'Amiral d'Estaing
75 116PARIS Cedex 16

Ref : n° 347